

	KELURAHAN KOTABARU					
1	Tanah Bangunan Kantor Pemerintah	01.11.04.01.	000001	376	2002	Kp. Cilendek Rt. 01/09

BADAN PERTANAHAN NASIONAL REPUBLIK INDONESIA



SERTIPIKAT (TANDA BUKTI HAK)

KANTOR PERTANAHAN
KABUPATEN / KOTA

TASIKMALAYA

1	0	•	2	9	•	0	3	•	0	5	•	4	•	0	0	0	1	7
---	---	---	---	---	---	---	---	---	---	---	---	---	---	---	---	---	---	---



BADAN PERTANAHAN NASIONAL REPUBLIK INDONESIA



SERTIPIKAT

HAK : PAKAI No. 00017

PROVINSI : JAWA BARAT
KABUPATEN / KOTA : TASIKMALAYA
KECAMATAN : CIBEUREUM
DESA / KELURAHAN : KOTABARU

KANTOR PERTANAHAN
KABUPATEN / KOTA

TASIKMALAYA

DAFTAR ISIAN 307

No. 11214/2015

DAFTAR ISIAN 208

No. 3914/2015

1	0	•	2	9	•	0	3	•	0	5	•	4	•	0	0	0	1	7
---	---	---	---	---	---	---	---	---	---	---	---	---	---	---	---	---	---	---

PENDAFTARAN - PERTAMA

Halaman :

a) HAK : Pakai No. : 00017 Desa / Kel. : Kotabaru Tgl. berakhirnya hak :	f) NAMA PEMEGANG HAK PEMERINTAH KOTA TASIKMALAYA Tanggal lahir / akta pendirian
b) NIB 10.29.03.05.02412 Letak Tanah Blok :	
c) ASAL HAK 1. Konversi 2. Pemberian hak Baru 3. Pemecahan / Pemisahan / Penggabungan bidang	g) PEMBUKUAN Tasikmalaya, Tgl. 23-03-2015 Kepala Kantor Pertanahan Kabupaten / Kota Tasikmalaya td
d) DASAR PENDAFTARAN 1. Daftar Isian 202 Tgl. No. 2. Surat Keputusan Kepala Kantor Pertanahan Kota Tasikmalaya Tgl. 30-12-2014 No. 30/HP/BPN-10.29/2014 3. Permohonan Pemecahan / Pemisahan / Penggabungan bidang Tgl. No.	Ir. KUSMANA NIP 19600303 198603 1 001
e) SURAT UKUR Tgl. 11-12-2014 No. 00239/Kotabaru /2014 Luas. 376 M² (Tiga ratus tujuh puluh enam meter persegi)	h) PENERBITAN SERTIPIKAT Tasikmalaya, Tgl. 23-03-2015 Kepala Kantor Pertanahan Kabupaten / Kota Tasikmalaya  Ir. KUSMANA NIP 19600303 198603 1 001
i) PENUNJUK Peta : 10.1-06.068.05 Lembar : 9 Kotak : A2 DI 301 No.8913/2015, Tgl.12-03-2015 Tanah yang dimohon adalah Tanah Negara bekas Milik Adat. Hak Pakai tersebut diberikan dalam jangka waktu selama dipakai/dipergunakan oleh pemohon untuk Kantor Kelurahan Kotabaru berlaku sejak tanggal didaftarkan pada Kantor Pertanahan Kota Tasikmalaya. Tanah yang diberikan dengan Hak Pakai tersebut, apabila akan diizinkan/dipindahkan haknya baik sebagian maupun seluruhnya kepada pihak lain harus dimintakan izin terlebih dahulu kepada pejabat yang berwenang sesuai dengan ketentuan yang berlaku.	

BT 277672

DAFTAR ISIAN 207

1	0	2	9	0	3	0	5	4	0	0	0	1	7
---	---	---	---	---	---	---	---	---	---	---	---	---	---

NIB : 10.29.03.05.02412

SURAT UKUR

Nomor : 00239/Kotabaru/2014

SEBIDANG TANAH TERLETAK DALAM

Provinsi : Jawa Barat

Kabupaten / Kota : Tasikmalaya

Kecamatan : Cibeureum

Desa / Kelurahan : Kotabaru

Peta : Pendaftaran Nomor Peta Pendaftaran : 49.1-06.068-05

Lembar : 9 Kotak : A2

Blok :

Keadaan Tanah : Sebidang tanah pekarangan di atasnya berdiri bangunan permanen (Kantor Kelurahan Kotabaru)


Tanda-tanda batas : Pagar tembok

Luas : 376 M² (Tiga ratus tujuh puluh enam meter persegi).

Penunjukan dan penetapan batas : Ditunjukkan oleh : IDI SUPRIADI HIDAYAT, SH, MSi untuk dan atas nama PEMKOT (Pemohon), dan penetapan batas oleh : ENKGUN YOGA PRANATA , NIP.19620919 199203 1 004 (Petugas Ukur)



SKALA 1 : 250

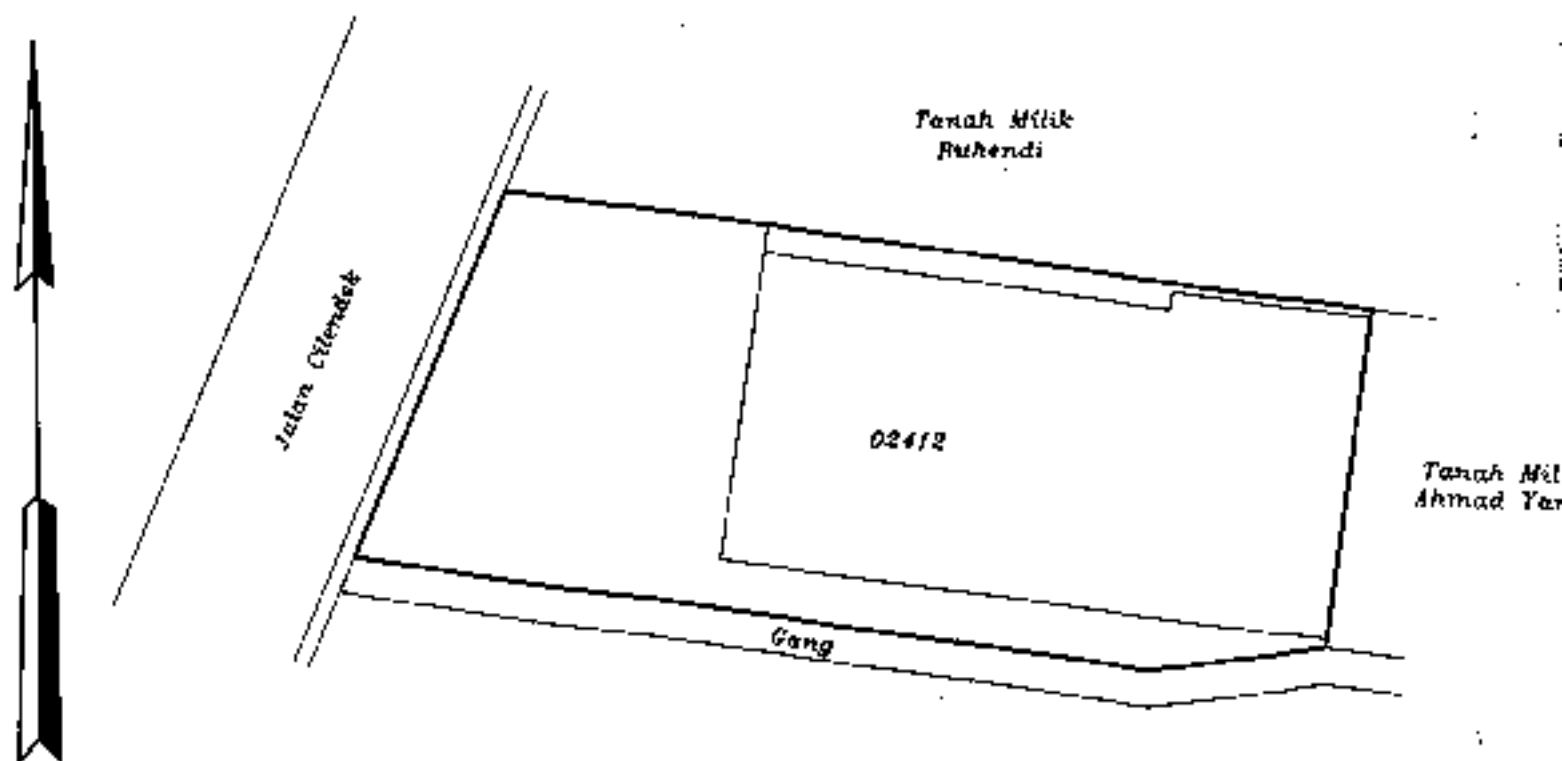

PENJELASAN : batas tanah ini



Surat Ukur ini menguraikan Tanah Milik Adat SPPT No 32.77.
(Peta Bidang No. 4604/2014/2014, Tgl. 11-12-2014)

Tanggal Penomoran Surat Ukur 11-12-2014

Tasikmalaya, 11-12-2014

Tasikmalaya, 23-03-2015

Kepala Seksi Survei, Pengukuran dan Pemetaan

Tasikmalaya

Ir. ENJANG HENDARSYAH

NIP 19610226 199003 1 002

NR 198603 1001

	Pemisahan
Lihat surat ukur	Penggabungan
	Penganti

Nomor :

Nomor hak :

[illegible]

Sisanya diuraikan dalam surat ukur Nomor :

Nomor hak :

Ketentuan P.P. 24 Tahun 1997 yang perlu diperhatikan

Pasal 17

- (3) Penempatan tanda-tanda batas termasuk pemeliharaannya, wajib dilakukan oleh pemegang hak atas tanah yang bersangkutan.

Pasal 32

- (1) Sertipikat merupakan surat tanda bukti hak yang berlaku sebagai alat pembuktian yang kuat mengenai data fisik dan data yuridis yang termuat di dalamnya, sepanjang data fisik dan data yuridis tersebut sesuai dengan data yang ada dalam surat ukur dan buku tanah hak yang bersangkutan.
- (2) Dalam hal atas suatu bidang tanah sudah diterbitkan sertipikat secara sah atas nama orang atau badan hukum yang memperoleh tanah tersebut dengan itikad baik dan secara nyata menguasainya, maka pihak lain yang merasa mempunyai hak atas tanah itu tidak dapat lagi menuntut pelaksanaan hak tersebut apabila dalam waktu 5 (lima) tahun sejak diterbitkannya sertipikat itu telah tidak mengajukan keberatan secara tertulis kepada pemegang sertipikat dan Kepala Kantor Pertanahan yang bersangkutan ataupun tidak mengajukan gugatan ke Pengadilan mengenai penguasaan tanah atau penerbitan sertipikat tersebut.

Pasal 36

- (1) Pemeliharaan data pendaftaran tanah dilakukan apabila terjadi perubahan pada data fisik atau data yuridis obyek pendaftaran tanah yang telah terdaftar.
- (2) Pemegang hak yang bersangkutan wajib mendaftarkan perubahan sebagaimana dimaksud pada ayat (1) kepada Kantor Pertanahan.

Pasal 40

- (1) Selambat-lambatnya 7 (tujuh) hari kerja sejak tanggal dilandatanganinya akta yang bersangkutan, PPAT wajib menyampaikan akta yang dibuatnya berikut dokumen-dokumen yang bersangkutan kepada Kantor Pertanahan untuk didaftar.
- (2) PPAT wajib menyampaikan pemberitahuan tertulis mengenai telah disampainya akta sebagaimana dimaksud pada ayat (1) kepada para pihak yang bersangkutan.

Pasal 42

- (1) Untuk pendaftaran peralihan hak karena pewarisan mengenai bidang tanah hak yang sudah didaftar dan hak milik atas satuan rumah susun sebagai yang diwajibkan menurut ketentuan sebagaimana dimaksud dalam pasal 36, wajib diserahkan oleh yang menerima hak atas tanah atau hak milik atas satuan rumah susun yang bersangkutan sebagai warisan kepada Kantor Pertanahan, sertipikat hak yang bersangkutan, surat kematian orang yang namanya dicatat sebagai pemegang haknya dan surat tanda bukti sebagai ahli waris.

