

**BADAN PERTANAHAN NASIONAL
REPUBLIK INDONESIA**



**SERTIPIKAT
(TANDA BUKTI HAK)**

**KANTOR PERTANAHAN
KABUPATEN / KOTA**

TASIKMALAYA

1	0	•	2	9	•	0	3	•	0	9	•	4	•	0	0	0	0	5
---	---	---	---	---	---	---	---	---	---	---	---	---	---	---	---	---	---	---



**BADAN PERTANAHAN NASIONAL
REPUBLIK INDONESIA****SERTIPIKAT**

HAK : PAKAI No. 00005

PROVINSI : JAWA BARAT
KABUPATEN / KOTA : TASIKMALAYA
KECAMATAN : CIBEUREUM
DESA / KELURAHAN : SETIANAGARA

KANTOR PERTANAHAN
KABUPATEN / KOTA
TASIKMALAYA

DAFTAR ISIAN 307
No. 31540 / 2012
DAFTAR ISIAN 208
No. 16837 / 2012

1 0 • 2 9 • 0 3 • 0 9 • 4 • 0 0 0 0 5

PENDAFTARAN - PERTAMA

Halaman :

a) HAK : PAKAI No. : 00005 Desa / Kel. : Setianagara Tgl. berakhirnya hak :	d) NAMA PEMEGANG HAK PEMERINTAH KOTA TASIKMALAYA Tanggal lahir / akta pendirian
b) NIB 10.29.03.09.00187 Letak Tanah Blok :	g) PEMBUKUAN Tasikmalaya, Tgl. 21-12-2012 Kepala Kantor Pertanahan Kabupaten / Kota Tasikmalaya ttd
c) ASAL HAK 1. Konversi 2. Pemberian hak Baru 3. Pemecahan / Pemisahan / Penggabungan bidang	d) DASAR PENDAFTARAN 1. Daftar Isian 2012 Tgl. No. 2. Surat Keputusan Kepala Kantor Pertanahan Kota Tasikmalaya Tgl. 18-09-2012 No. 05/HP/BPN.32.78/2012 3. Pemecahan / Pemecahan / Pemisahan / Penggabungan bidang Tgl. No.
e) SURAT UKUR Tgl. 27-11-2012 No. 00053/Setianagara/2012 Luas 11.500 MP (Sebelas ribu lima ratus meter persegi)	b) PENERBITAN SERTIPIKAT Tasikmalaya, Tgl. 21-12-2012 Kepala Kantor Pertanahan Kabupaten / Kota Tasikmalaya  AKUR NURASA NIP 19570701 198303 1 005
i) PENUNJUK Petunjuk Pendaftaran 49.1-05.008-09, Lembar : 8, Kotak : C2 Dt. 301/196.13.372/2012, Tgl. 23-09-2012 Tanah yang dimaksud adalah Tanah Cakrawala Pemerintah Desa Setianagara. Hak Pakai tersebut diberikan dalam jangka waktu selama dipakai/dipergunakan oleh pemohon untuk Tempat Pemukiman Umum. Apabila Tanah akan dialihkan/dipindahkan haknya oleh pemohon baik sebagian maupun seluruhnya kepada pihak lain harus dimintakan izin terlebih dahulu kepada pejabat yang berwenang sesuai ketentuan yang berlaku.	

BL 522399

DAFTAR ISIAN 207

10.29.03.09.4.00005

NIB : 10.29.03.09.00187

SURAT UKUR

Nomor : 00053/Setianagara/2012

SEBIDANG TANAH TERLETAK DALAM

Provinsi : Jawa Barat

Kabupaten / Kota : Tasikmalaya

Kecamatan : Cibacureum

Desa / Kelurahan : Setianagara

Peta : Peta Pendaftaran

Nomor Peta Pendaftaran : 49.1-06.068-09

Lembar : 8 Kotak : C2

Keadaan Tanah : Sebidang tanah dipergunakan untuk Pemakaman


Tanda-tanda batas : Patok Beton

Luas : 11500 M² (Sebelas ribu lima ratus meter persegi)

Penunjukan dan penetapan batas : Ditunjukkan oleh KOSIM bertindak untuk dan atas nama
PEMERINTAH KOTA TASIKMALAYA (Pemohon) dan penetapan batas oleh ENGGUN YOGA
PRANATA, NIP. 19620919-199203 1 004 (Petugas Ukur)



SKALA 1 : 1000

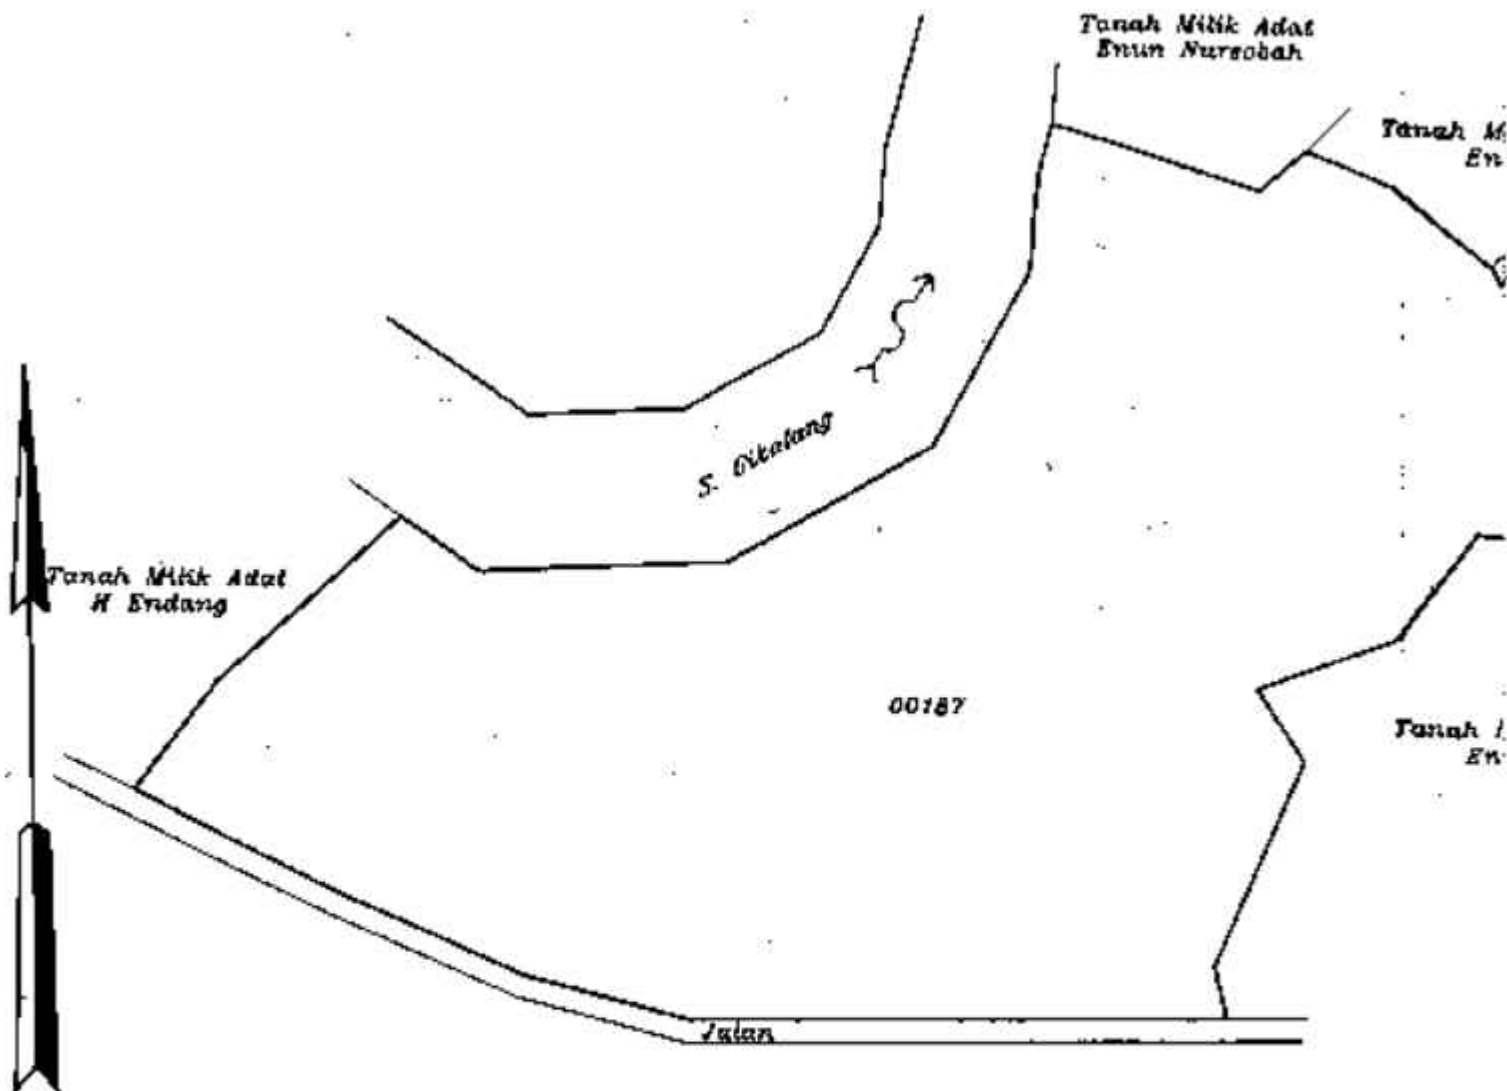


PENJELASAN : batas tanah ini

Sk Adat
p

Tanah Milik Adat
H Alimin

ilik Adat
ang

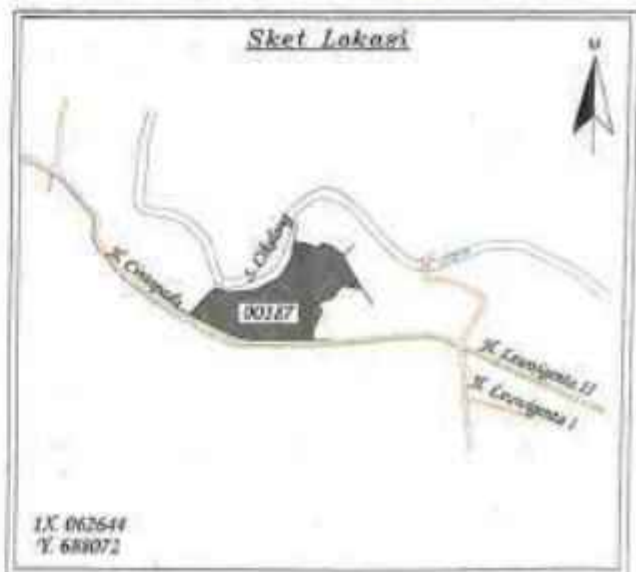

Hal lain - lain : Surat Ukur ini berdasarkan Keputusan Kepala Kantor Pertanahan Kota Tasikmalaya Nomor

05/HP/BPN.32.78/2012 Tanggal 18-09-2012 (Peta Bidang No.2580/2011 Tanggal 15-11-2011)

Di. 303 No. 7796 Tanggal. 25-09-2012

Di. 307 No. 29686 Tanggal. 27-11-2012

Daftar Isian 302 tgl. 01-11-2011 No. 4537

Daftar Isian 307 tgl. 15-11-2011 No. 27224

Tanggal Penomoran Surat Ukur 27-11-2012

UNTUK SERTIPIKAT

Tasikmalaya, 27-11-2012

Tasikmalaya, 21-12-2012

Kepala Seksi Survei, Pengukuran dan Pemetaan

Kepala Kantor Pertanahan



Kantor Pertanahan

Kabupaten / Kota
Tasikmalaya

ttd

IRWAN, ST. M.Si

NIP 19620216 198503 1 008

Lihat surat ukur Pemisahan
Penggabungan
Pengganti

Nomor :

Nomor hak :

Dikeluarkan surat ukur		Luas	Nomor hak	Sisa luas
Tanggal	Nomor			

Sisanya diuraikan dalam surat ukur Nomor :

Nomor hak :

Ketentuan P.P. 24 Tahun 1997 yang perlu diperhatikan

Pasal 17

- (3) Penempatan tanda-tanda batas termasuk pemeliharaannya, wajib dilakukan oleh pemegang hak atas tanah yang bersangkutan.

Pasal 32

- (1) Sertipikat merupakan surat tanda bukti hak yang berlaku sebagai alat pembuktian yang kuat mengenai data fisik dan data yuridis yang termuat di dalamnya, sepanjang data fisik dan data yuridis tersebut sesuai dengan data yang ada dalam surat ukur dan buku tanah hak yang bersangkutan.
- (2) Dalam hal atas suatu bidang tanah sudah diterbitkan sertipikat secara sah atas nama orang atau badan hukum yang memperoleh tanah tersebut dengan itikad baik dan secara nyata menguasainya, maka pihak lain yang merasa mempunyai hak atas tanah itu tidak dapat lagi menuntut pelaksanaan hak tersebut apabila dalam waktu 5 (lima) tahun sejak diterbitkannya sertipikat itu telah tidak mengajukan keberatan secara tertulis kepada pemegang sertipikat dan Kepala Kantor Pertanahan yang bersangkutan ataupun tidak mengajukan gugatan ke Pengadilan mengenai penguasaan tanah atau penerbitan sertipikat tersebut.

Pasal 36

- (1) Pemeliharaan data pendaftaran tanah dilakukan apabila terjadi perubahan pada data fisik atau data yuridis obyek pendaftaran tanah yang telah terdaftar.
- (2) Pemegang hak yang bersangkutan wajib mendaftarkan perubahan sebagaimana dimaksud pada ayat (1) kepada Kantor Pertanahan.

Pasal 40

- (1) Selambat-lambatnya 7 (tujuh) hari kerja sejak tanggal dilandatanganinya akta yang bersangkutan, PPAT wajib menyampaikan akta yang dibuatnya beserta dokumen-dokumen yang bersangkutan kepada Kantor Pertanahan untuk didaftar.
- (2) PPAT wajib menyampaikan pemberitahuan tertulis mengenai telah disampaikannya akta sebagaimana dimaksud pada ayat (1) kepada para pihak yang bersangkutan.

Pasal 42

- (1) Untuk pendaftaran peralihan hak karena pewarisan mengenai bidang tanah hak yang sudah didaftar dan hak milik atas satuan rumah susun sebagai yang diwajibkan menurut ketentuan sebagaimana dimaksud dalam pasal 36, wajib diserahkan oleh yang menerima hak atas tanah atau hak milik atas satuan rumah susun yang bersangkutan sebagai warisan kepada Kantor Pertanahan, sertipikat hak yang bersangkutan, surat kematian orang yang namanya dicatat sebagai pemegang haknya dan surat tanda bukti sebagai ahli waris.



