

**BADAN PERTANAHAN NASIONAL
REPUBLIK INDONESIA**



**SERTIPIKAT
(TANDA BUKTI HAK)**

**KANTOR PERTANAHAN
KABUPATEN / KOTA**

TASIKMALAYA

1	0	•	2	9	•	0	1	•	0	5	•	4	•	0	0	0	1	1
---	---	---	---	---	---	---	---	---	---	---	---	---	---	---	---	---	---	---



**BADAN PERTANAHAN NASIONAL
REPUBLIK INDONESIA****SERTIPIKAT**

RAK : PAKAI No. 00011

PROVINSI : JAWA BARAT
KABUPATEN / KOTA : TASIKMALAYA
KECAMATAN : KAWALU
DESA / KELURAHAN : TALAGASARI

KANTOR PERTANAHAN
KABUPATEN / KOTA
TASIKMALAYA

DAFTAR ISIAN 307

No. 7020/2016

DAFTAR ISIAN 208

No. 3336/2016

1 • 0 • 2 • 9 • 0 • 1 • 3 • 5 • 4 • 6 • 2 • 1

PENDAFTARAN - PERTAMA

Halaman :

a) HAK : Pakai No. : 00011 Dasa / Kel. : Talagasari Tgl. berakhirnya hak : —	f) NAMA PEMEGANG HAK PEMERINTAH KOTA TASIKMALAYA Tanggal lahir / akta kelahiran
b) NIB : 10.29.01.05.00574 Letak Tanah Blok : —	
c) ASAL HAK 1. Konversi 2. Pemberian hak Baru 3. Pemecahan / Pembagian / Penggabungan bidang	g) PEMBUKUAN Tasikmalaya, Tgl. 15-03-2016 Kepala Kantor Pertanahan Kabupaten / Kota Tasikmalaya  ttd
d) DASAR PENDAFTARAN 1. Daftar Isian 202 Tgl. — No. — 2. Surat Keputusan Kepala Kantor Pertanahan Kota Tasikmalaya Tgl. 14-12-2015 No. 54/HK/PTN-10.29/2015 3. Pemecahan Pemecahan / Pembagian / Penggabungan bidang Tgl. — No. —	h) PENERBITAN SERTIPIKAT Tasikmalaya, Tgl. 15-03-2016 Kepala Kantor Pertanahan Kabupaten / Kota Tasikmalaya  Ir. KUSMANA NIP. 19600303 198603 1 001
e) SURAT UKUR Tgl. 11-03-2016 No. 00132/Talagasari/2016 Luas : 1 098 M² (Seribu sembilan ratus delapan puluh meter persegi)	Ir. KUSMANA NIP. 19600303 198603 1 001
i) PENUNJUK DL 101 No.4306/2016, Tgl.08-03-2016 Peta : 49.1-05.007-13, Lembar : 7, Kotak : B4 Berdasarkan Hasil Pemeriksaan Tim Penilai Tanah tanggal 26-12-2015 Nomor : 1524/HK/PTD/HPT/2015, Dimana Atas Pemukiman Lapangan tanggal 18-12-2015 surat keterangan bahwa hak Pakai tersebut diberikan dalam jangka waktu dimana dipakainya digunakan oleh pemohon untuk Hengman Kantor Kecamatan Kawali, berlaku sejak tanggal diadilkan pada Kantor Pertanahan Kota Tasikmalaya. Tanah yang diberikan dengan Hak Pakai tersebut, apabila akan diadilkan/dipindahkan maka hak sebagai maupun seluruhnya kepada pihak lain harus dimintakan izin terlebih dahulu kepada pejabat yang berwenang sesuai dengan ketentuan yang berlaku.	

0	2	9	0	1	0	3	4	0	0	0	1
---	---	---	---	---	---	---	---	---	---	---	---

NIB : 10.29.01.05.00574

SURAT UKUR

Nomor : 00132/Talagasari/2016

SEBIDANG TANAH TERLETAK DALAM


Provinsi : Jawa Barat
Kabupaten/ Kota : Tasikmalaya
Kecamatan : Kawalu
Desa/ Kelurahan : Talagasari
Peta : Pendaftaran Nomor Peta Pendaftaran : 49.1-05.067-13
Lembar : 7 Kotak : B4
Blok :
Kondisi Tanah : Sebidang tanah pekarangan diatasnya terdapat bangunan permanen (Kantor Kecamatan)
Tanda-tanda batas : Tembok

Luas : 1098 M² (Seribu sembilan puluh delapan meter persegi)

Penunjukan dan penetapan batas : Ditunjukkan oleh : IDI SUPRIADI HIDAYAT, SH. M.Si untuk dan atas nama PEMKOT (Pemohon), dan penetapan batas oleh : ENKGUN YOGA PRANATA, NIP.19620919 199203 1 004 (Petugas Ukur)



SKALA 1 : 1000

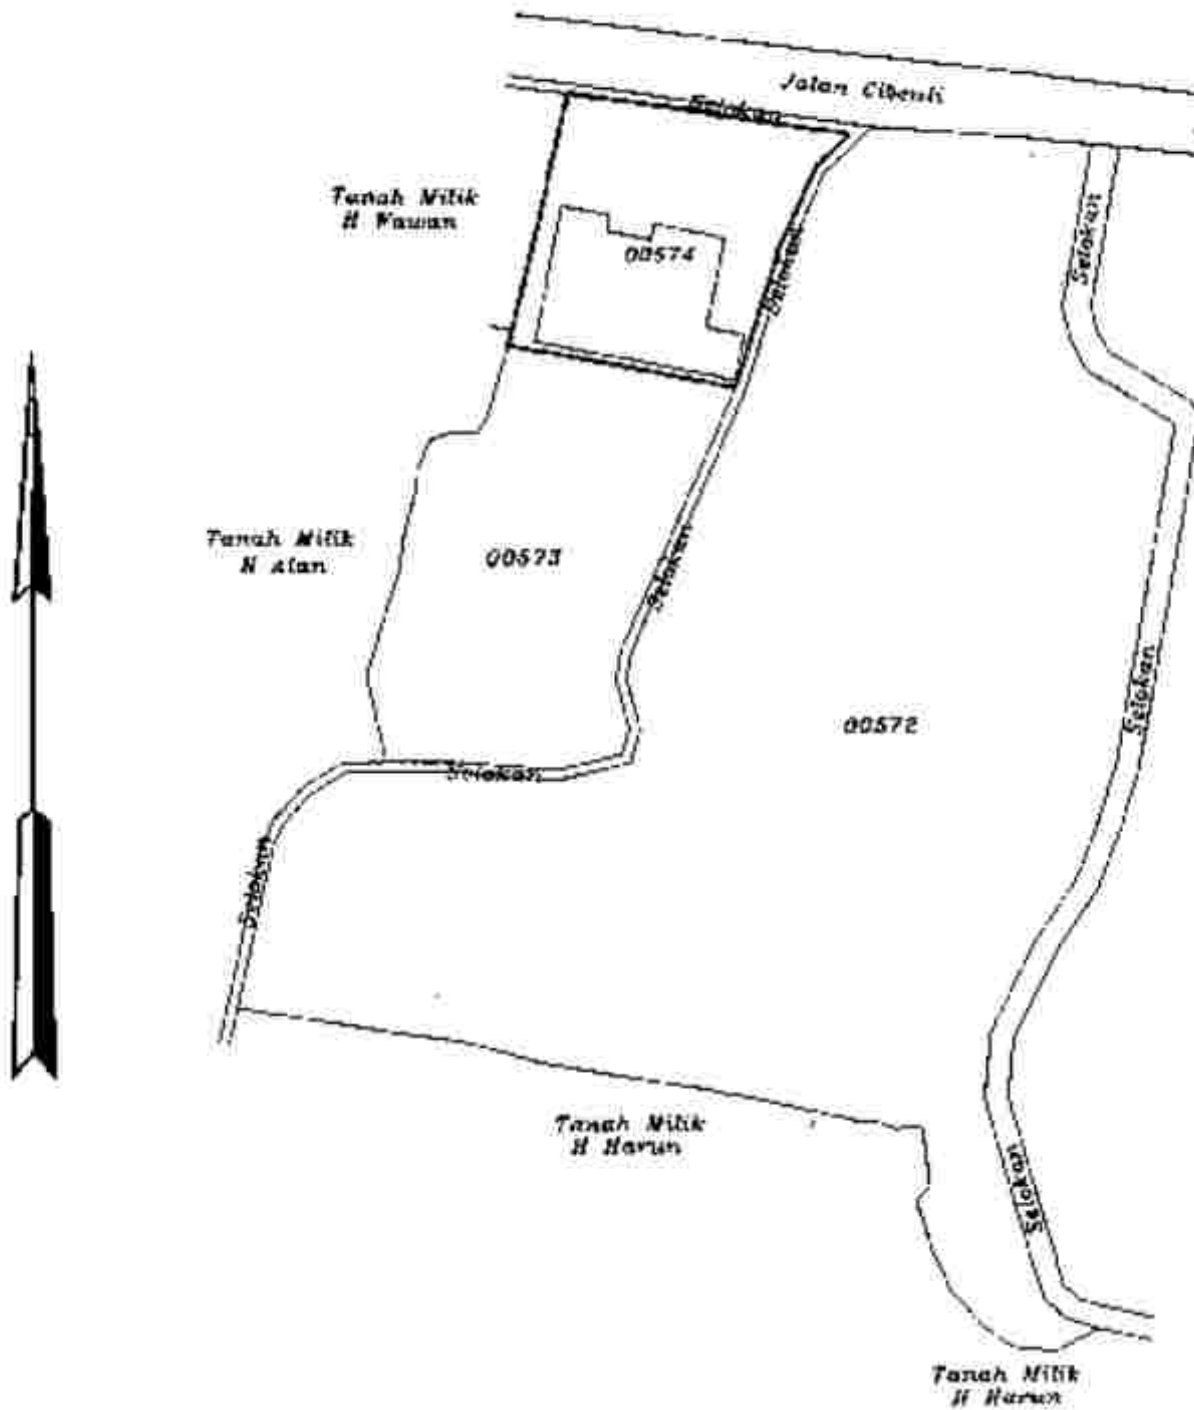

PENJELASAN : batas tanah ini

Daftar Isian ³⁰³ 302 tgl. 08-03-2016 No. 2262

Daftar Isian 307 tgl. 11-03-2016 No. 6770

Tanggal Penomoran Surat Ukur 11-03-2016

UNTUK SERTIPIKAT

Tasikmalaya, 11-03-2016

Tasikmalaya, 15-03-2016

Kepala Seksi Survei, Pengukuran dan Pemetaan



Kantor Pertanahan
Kabupaten / Kota
Tasikmalaya

titid

Ir. ENJIANG HENDARSYAH

NIP 19610226 199003 1 002

Lihat surat ukur Pemisahan
Penggabungan
Pengganti

Nomor :

Nomor hak :

Dikeluarkan surat ukur		Luas	Nomor hak	Sisa luas
Tanggal	Nomor			

Sisanya diuraikan dalam surat ukur Nomor :

Nomor hak :

Ketentuan P.P. 24 Tahun 1997 yang perlu diperhatikan

Pasal 17

- (3) Penempatan tanda-tanda batas termasuk pemeliharaannya, wajib dilakukan oleh pemegang hak atas tanah yang bersangkutan.

Pasal 32

- (1) Sertipikat merupakan surat tanda bukti hak yang berlaku sebagai alat pembuktian yang kuat mengenai data fisik dan data yuridis yang termuat di dalamnya, sepanjang data fisik dan data yuridis tersebut sesuai dengan data yang ada dalam surat ukur dan buku tanah hak yang bersangkutan.
- (2) Dalam hal atas suatu bidang tanah sudah diterbitkan sertipikat secara sah atas nama orang atau badan hukum yang memperoleh tanah tersebut dengan ikhtisad baik dan sepers nyata menguasainya, maka pihak lain yang merasa mempunyai hak atas tanah itu tidak dapat lagi menuntut pelaksanaan hak tersebut apabila dalam waktu 5 (lima) tahun sejak diterbitkannya sertipikat itu telah tidak mengajukan keberatan secara tertulis kepada pemegang sertipikat dan Kepala Kantor Pertanahan yang bersangkutan ataupun tidak mengajukan gugatan ke Pengadilan mengenai penguasaan tanah atau penerbitan sertipikat tersebut.

Pasal 36

- (1) Pemeliharaan data pendaftaran tanah dilakukan apabila terjadi perubahan pada data fisik atau data yuridis objek pendaftaran tanah yang telah terdaftar.
- (2) Pemegang hak yang bersangkutan wajib memberitukan perubahan sebagaimana dimaksud pada ayat (1) kepada Kantor Pertanahan.

Pasal 40

- (1) Selama lamanya 7 (tujuh) hari kerja sejak tanggal diterbitkannya akta yang bersangkutan, PPAT wajib menyampaikan akta yang diuastinya beserta dokumen-dokumen yang bersangkutan kepada Kantor Pertanahan untuk didaftar.
- (2) PPAT wajib menyampaikan pemberitahuan tertulis mengenai telah disampaikan akta sebagaimana dimaksud pada ayat (1) kepada para pihak yang bersangkutan.

Pasal 42

- (1) Untuk pendaftaran pemeliharaan hak karena pemisahan mengenai bidang tanah hak yang sudah terdaftar dan hak milik atas suatu rumah susun sebagai yang diwajibkan menurut ketentuan sebagaimana dimaksud dalam pasal 36, wajib diserahkan oleh yang mempunyai hak atas tanah atau hak milik atas sebuah rumah susun yang bersangkutan sebagai warisan kepada Kantor Pertanahan, sertipikat hak yang bersangkutan, surat kematian orang yang namanya dicatat sebagai pemegang haknya, dan surat tanda bukti sebagai ahli waris.



