



SHP No. 00020 Tgl. 01-07-2020

Luas: 5.940 M²

Komplek Perkantoran Kec. Cihideung

**KEMENTERIAN AGRARIA DAN TATA RUANG /
BADAN PERTANAHAN NASIONAL
REPUBLIK INDONESIA**



**SERTIPIKAT
(TANDA BUKTI HAK)**

**KANTOR PERTANAHAN
KABUPATEN / KOTA**

TASIKMALAYA

1	0	•	2	9	•	0	5	•	0	6	•	4	•	0	0	0	2	0
---	---	---	---	---	---	---	---	---	---	---	---	---	---	---	---	---	---	---

**KEMENTERIAN AGRARIA DAN TATA RUANG /
BADAN PERTANAHAN NASIONAL
REPUBLIK INDONESIA**



SERTIPIKAT

HAK : **PAKAI** No. 00020

PROVINSI : **JAWA BARAT**

~~KABUPATEN~~ / KOTA : **TASIKMALAYA**

KECAMATAN : **CIHIDEUNG**

~~DESA~~ / KELURAHAN : **ARGASARI**

KANTOR PERTANAHAN
~~KABUPATEN~~ / KOTA

TASIKMALAYA

DAFTAR ISIAN 307

No. 18082/2020

DAFTAR ISIAN 208

No. 9927/2020

1	0	•	2	9	•	0	5	•	0	6	•	4	•	0	0	0	2	0
---	---	---	---	---	---	---	---	---	---	---	---	---	---	---	---	---	---	---

PENDAFTARAN - PERTAMA

Halaman :

a) HAK : Pakai No. : 00020 Desa / Kel : Argasari Tgl. berakhirnya hak : ==	f) NAMA PEMEGANG HAK PEMERINTAH KOTA TASIKMALAYA Tanggal lahir / akta pendirian
b) NIB 10.29.05.06.01613 Letak Tanah Blok :	
c) ASAL HAK 1. Konversi 2. Pemberian Hak 3. Pemecahan / Pemisahan / Penggabungan bidang	g) PEMBUKUAN Tasikmalaya, 01-07-2020 Kepala Kantor Pertanahan Kabupaten / Kota Tasikmalaya ttd
d) DASAR PENDAFTARAN 1. Daftar Isian 202 Tgl. No. 2. Surat Keputusan Kepala Kantor Pertanahan Kota Tasikmalaya Tgl. 19-12-2019 No. 50/HP/BPN-10.29/2019 3. Permohonan Pemecahan / Pemisahan / Penggabungan bidang Tgl. No.	h) PENERBITAN SERTIPIKAT Tasikmalaya, 01-07-2020 Kepala Kantor Pertanahan Kabupaten / Kota Tasikmalaya  RISWAN SUHENDI, SH. NIP 19631202 199103 1 002
e) SURAT UKUR Tgl. 26-06-2020 No. 00862/Argasari/2020 Luas : 5.940 M² (Lima ribu sembilan ratus empat puluh meter persegi)	RISWAN SUHENDI, SH. NIP 19631202 199103 1 002
i) PENUNJUK DI. 301 : 5862/2020 Tanggal 17-06-2020 Peta Pendaftaran : 49.1-05.068-13, Lembar : 8, Kotak : C4 Tanah yang dimohon adalah Tanah Negara bekas Tanah Hak Pakai No. 3/Argasari. Hak Pakai tersebut diberikan dalam jangka waktu selama dipakai/dipergunakan oleh pemohon untuk Komplek Perkantoran Kecamatan Cihideung berlaku sejak tanggal didaftarkan pada Kantor Pertanahan Kota Tasikmalaya. Tanah yang diberikan dengan Hak Pakai tersebut, apabila akan dialihkan/dipindahkan haknya baik sebagian maupun seluruhnya kepada pihak lain harus dimintakan izin terlebih dahulu kepada pejabat yang berwenang sesuai dengan ketentuan yang berlaku.	

1	0	•	2	9	•	0	5	•	0	6	•	4	•	0	0	0	2	0
---	---	---	---	---	---	---	---	---	---	---	---	---	---	---	---	---	---	---

NIB : 10.29.05.06.01613

SURAT UKUR

Nomor : 00862/Argasari/2020

SEBIDANG TANAH TERLETAK DALAM

Provinsi : Jawa Barat

Kabupaten / Kota : Tasikmalaya

Kecamatan : Cihideung

Desa / Kelurahan : Argasari

Peta : Pendaftaran

Nomor Peta Pendaftaran : 49,1-05,068-13

Lembar : 8

Kotak : C4

Blok :

Keadaan Tanah : Sebidang tanah pekarangan di atasnya berdiri bangunan permanen

Tanda-tanda batas : Tembok


Luas : 5940 M² (Lima ribu sembilan ratus empat puluh meter persegi)

Penunjukan dan penetapan batas : Ditunjukkan oleh : OTONG S. untuk dan atas nama PEMERINTAH
KOTA TASIKMALAYA (Pemohon), dan penetapan batas oleh :
ENGKUN YOGA PRANATA , NIP.19620919 199203 1 004
(Petugas Ukur)





SKALA 1 : 1000

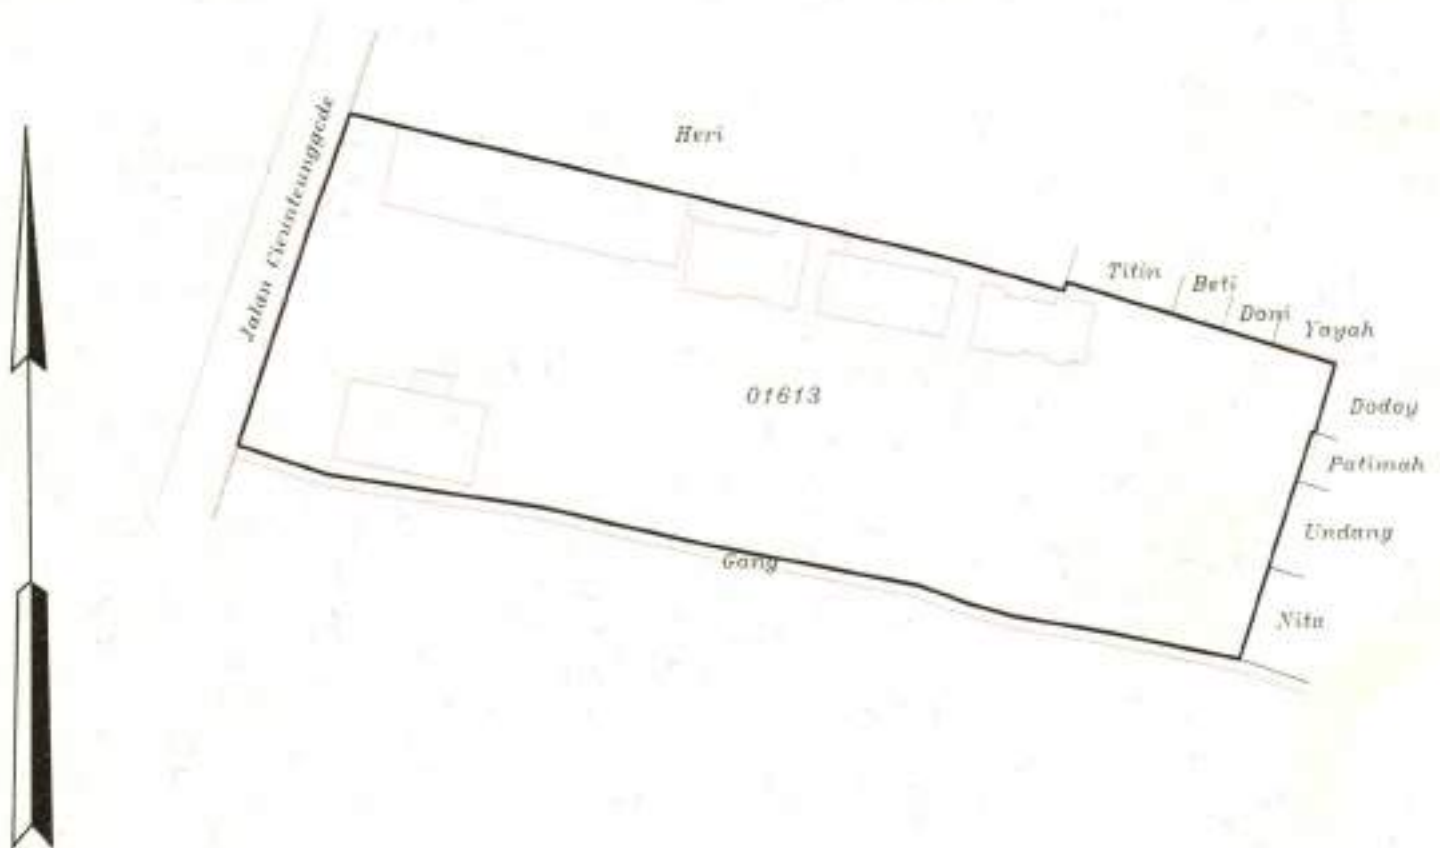

PENJELASAN : _____ batas tanah ini

Ketentuan P.P. 24 Tahun 1997 yang perlu diperhatikan

Pasal 17

- (3) Penempatan tanda-tanda batas termasuk pemeliharannya, wajib dilakukan oleh pemegang hak atas tanah yang bersangkutan.

Pasal 32

- (1) Sertipikat merupakan surat tanda bukti hak yang berlaku sebagai alat pembuktian yang kuat mengenai data fisik dan data yuridis yang termuat di dalamnya, sepanjang data fisik dan data yuridis tersebut sesuai dengan data yang ada dalam surat ukur dan buku tanah hak yang bersangkutan.
- (2) Dalam hal atas suatu bidang tanah sudah diterbitkan sertipikat secara sah atas nama orang atau badan hukum yang memperoleh tanah tersebut dengan itikad baik dan secara nyata menguasainya, maka pihak lain yang merasa mempunyai hak atas tanah itu tidak dapat lagi menuntut pelaksanaan hak tersebut apabila dalam waktu 5 (lima) tahun sejak diterbitkannya sertipikat itu telah tidak mengajukan keberatan secara tertulis kepada pemegang sertipikat dan Kepala Kantor Pertanahan yang bersangkutan ataupun tidak mengajukan gugatan ke Pengadilan mengenai penguasaan tanah atau penerbitan sertipikat tersebut.

Pasal 36


- (1) Pemeliharaan data pendaftaran tanah dilakukan apabila terjadi perubahan pada data fisik atau data yuridis obyek pendaftaran tanah yang telah terdaftar.
- (2) Pemegang hak yang bersangkutan wajib mendaftarkan perubahan sebagaimana dimaksud pada ayat (1) kepada Kantor Pertanahan.

Pasal 40

- (1) Selambat-lambatnya 7 (tujuh) hari kerja sejak tanggal ditandatanganinya akta yang bersangkutan, PPAT wajib menyampaikan akta yang dibuatnya berikut dokumen-dokumen yang bersangkutan kepada Kantor Pertanahan untuk didaftar.
- (2) PPAT wajib menyampaikan pemberitahuan tertulis mengenai telah disampaikannya akta sebagaimana dimaksud pada ayat (1) kepada para pihak yang bersangkutan.

Pasal 42

- (1) Untuk pendaftaran peralihan hak karena pewarisan mengenai bidang tanah hak yang sudah didaftar dan hak milik atas satuan rumah susun sebagai yang diwajibkan menurut ketentuan sebagaimana dimaksud dalam pasal 36, wajib diserahkan oleh yang menerima hak atas tanah atau hak milik atas satuan rumah susun yang bersangkutan sebagai warisan kepada Kantor Pertanahan, sertipikat hak yang bersangkutan, surat kematian orang yang namanya dicatat sebagai pemegang haknya dan surat tanda bukti sebagai ahli waris.

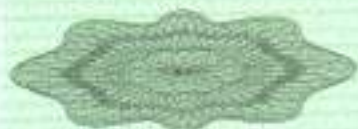

Hal lain - lain: Surat Ukur ini menguraikan Tanah Negara bekas Hak Pakai No. 00003/Argasari Gambar
Situasi No. 2310/1984, Tgl. 02-08-1984 (PBT No. 46/2019, Tgl. 21-01-2019)
Kepala Sub Seksi Pengukuran & Pemetaan Kadastral : Nandang Supriatna, S.SIT, MH.
NIP : 197012161994031005

Daftar Isian 302 tgl. 14-12-2016 No. 5447

Daftar Isian 307 tgl. 26-06-2020 No. 17569

Tanggal Penomoran Surat Ukur 26-06-2020

UNTUK SERTIPIKAT

Tasikmalaya, 26-06-2020

Tasikmalaya, 01-07-2020

Kepala Seksi Infrastruktur Pertanian

Kepala Kantor Pertanian

Kabupaten / Kota

Tasikmalaya



Kantor Pertanian

Kabupaten / Kota

Tasikmalaya

ttd

DEDE SUMARNA, S.SiT

NIP 19720327 199303 1 001

Lihat Surat Ukur Pemisahan
Penggabungan
Pengganti

Nomor :

Nomor Hak :

Dikeluarkan Surat Ukur		Luas	Nomor Hak	Sisa luas
Tanggal	Nomor			

Sisanya diuraikan dalam Surat Ukur Nomor : Nomor Hak :