

**BADAN PERTANAHAN NASIONAL
REPUBLIK INDONESIA**



**SERTIPIKAT
(TANDA BUKTI HAK)**

**KANTOR PERTANAHAN
KABUPATEN/ KOTA**

TASIKMALAYA

10 • 29 • 10 • 06 • 4 • 00002 ✓

BADAN PERTANAHAN NASIONAL REPUBLIK INDONESIA



SERTIPIKAT

HAK : PAKAI No. 00002 /

PROPINSI : JAWA BARAT /

~~KABUPATEN~~ / KOTA : TASIKMALAYA /

KECAMATAN : KAWALI /

~~DESA~~ KELURAHAN : TANJUNG /

KANTOR PERTANAHAN
~~KABUPATEN~~ / KOTA

TASIKMALAYA /

DAFTAR ISIAN 307
No. 8185/2008

DAFTAR ISIAN 208
No. 3840/2008

10 • 29 • 10 • 06 • 4 • 00002 /

PENDAFTARAN - PERTAMA

Halaman :

F

a) HAK : PAKAI ✓ No. : 00002 ✓ Desa / Kel. : Tanjung ✓ Tgl. berakhirnya hak :	f) NAMA PEMEGANG HAK = PEMERINTAH KOTA TASIKMALAYA. = Tanggal lahir / akta pendirian
b) NIB 10.29.10.06.00234 ✓ Letak Tanah Blok : Citaniang.	
c) ASAL HAK 1. Konversi 2. Pemberian hak 3. Pemecahan / Pemisahan / Penggabungan bidang	g) PEMBUKUAN Tasikmalaya, tgl. <u>30-05-2008</u> Kepala Kantor Pertanahan Kabupaten Kota Tasikmalaya ✓ ttd
d) DASAR PENDAFTARAN 1. Daftar Isian 202 Tgl. No. 2. Surat Keputusan Kepala Kantor Pertanahan Kota Tasikmalaya. ✓ Tgl. 24-03-2008 No. 54-320.2-32.78-2008 ✓ 3. Pemohonan Pemecahan / Pemisahan / Penggabungan bidang Tgl. No.	 H. A. BUDI RACHMAN, SH. ✓ NIP 010 153 269
e) SURAT UKUR Tgl. 31-03-2008 ✓ No. 00039/Tanjung/2008 ✓ Luas, 328 M² (Tigaratus duapuluh delapan meter persegi) ✓	h) PENERBITAN SERTIPIKAT Tasikmalaya, tgl. <u>30-05-2008</u> Kepala Kantor Pertanahan  Kabupaten Kota Tasikmalaya ✓  H. A. BUDI RACHMAN, SH. ✓ NIP 010 153 269
i) PENUNJUK D.I. 301 No : 2502/2008 ✓ Peta Blok: 09 Lembar ke : 01 NOP : 183,182 seb. ✓ Penggunaan tanah Kantor Kelurahan. Apabila tanah tersebut akan dialihkan / dipindahkan haknya kepada pihak lain, harus dimintakan izin terlebih dahulu kepada Pejabat yang berwenang.	

10.29.10.06.4.00002

NIB : 10.29.10.06.00234

SURAT UKUR

Nomor : 00039/Tanjung/2008

SEBIDANG TANAH TERLETAK DALAM

Propinsi : Jawa Barat

~~Kabupaten~~/ Kota : Tasikmalaya

Kecamatan : Kawalu

~~Desa~~/Kelurahan : TanjungPeta : Blok 09 NOP 183, 182 ^{se} Nomor Peta Pendaftaran :

Lembar : 01 Kotak :


Blok Citaniang

Keadaan Tanah : Sebidang tanah pekarangan di atasnya berdiri sebuah bangunan permanen yang
dipergunakan untuk kantor kelurahan.


Tanda-tanda batas : Berupa

Luas : 328 M² (Tiga ratus dua puluh delapan meter persegi)

Penunjukan dan penetapan batas : Ditunjukkan oleh : USMAN untuk atas nama PEMKOT

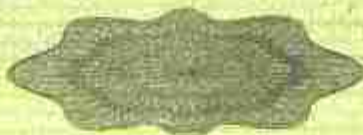

SKALA 1 : 250

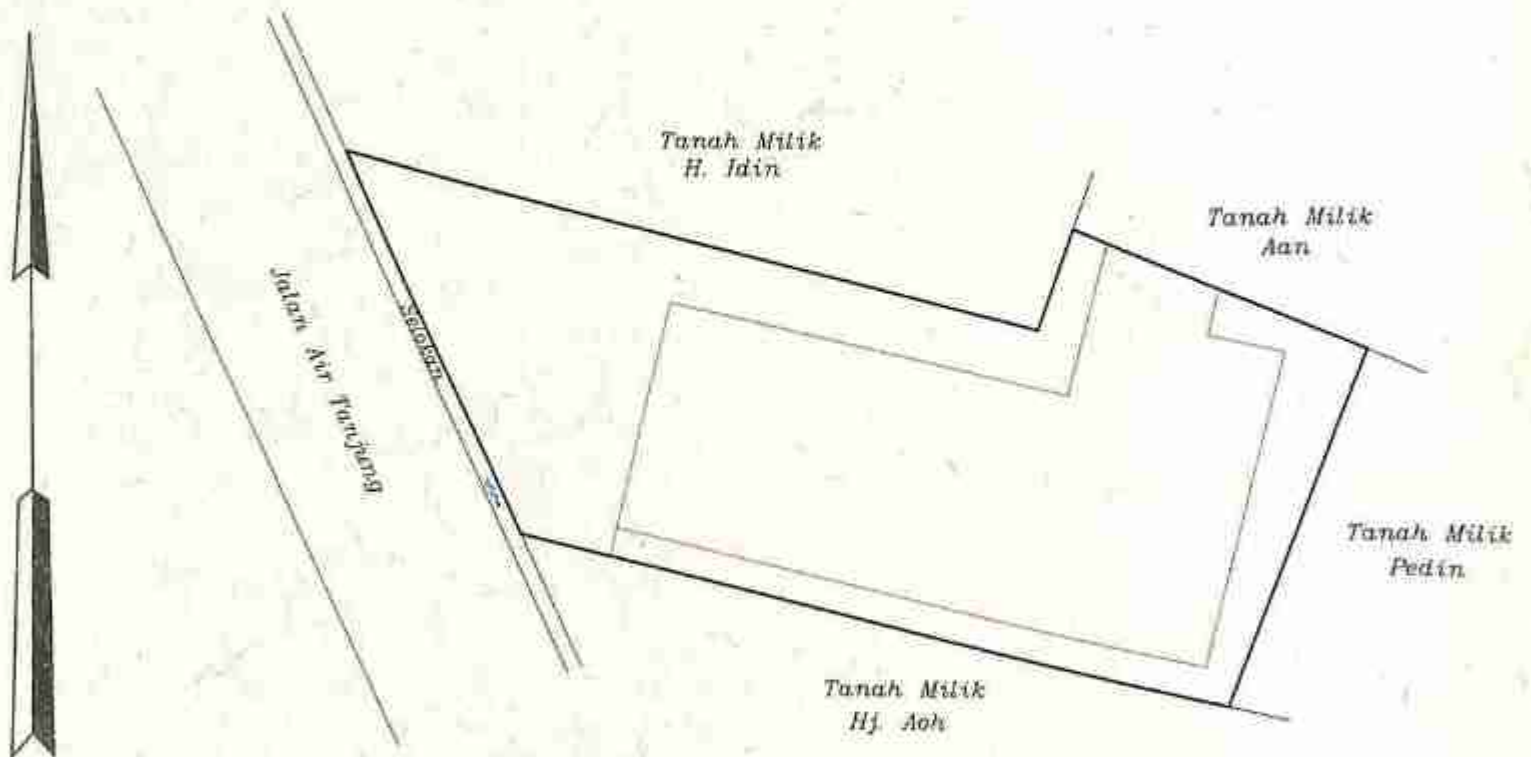

PENJELASAN : batas tanah ini

Nomor hak :

Ketentuan P.P. 24 Tahun 1997 yang perlu diperhatikan

Pasal 17

- (3) Penempatan tanda-tanda batas termasuk pemeliharannya wajib dilakukan oleh pemegang hak atas tanah yang bersangkutan.

Pasal 32

- (1) Sertifikat merupakan surat tanda bukti hak yang berlaku sebagai alat pembuktian yang kuat mengenai data fisik dan data yuridis yang termuat di dalamnya, sepanjang data fisik dan data yuridis tersebut sesuai dengan data yang ada dalam surat ukur dan buku tanah hak yang bersangkutan.
- (2) Dalam hal atas suatu bidang tanah sudah diterbitkan sertifikat secara sah atas nama orang atau badan hukum yang memperoleh tanah tersebut dengan itikad baik dan secara nyata menguasainya, maka pihak lain yang merasa mempunyai hak atas tanah itu tidak dapat lagi menuntut pelaksanaan hak tersebut apabila dalam waktu 5 (lima) tahun sejak diterbitkan sertifikat itu tidak mengajukan keberatan secara tertulis kepada pemegang sertifikat dan Kepala Kantor Pertanahan yang bersangkutan ataupun tidak mengajukan gugatan ke Pengadilan mengenai penguasaan tanah atau penorbitan sertifikat tersebut.

Pasal 36

- (1) Pemeliharaan data pendaftaran tanah dilakukan apabila terjadi perubahan pada data fisik atau data yuridis obyek pendaftaran tanah yang telah terdaftar.
- (2) Pemegang hak yang bersangkutan wajib mendaftarkan perubahan sebagaimana dimaksud pada ayat (1) kepada Kantor Pertanahan.

Pasal 40

- (1) Selambat-lambatnya 7 (tujuh) hari kerja sejak tanggal ditandatanganinya akta yang bersangkutan, PPAT wajib menyampaikan akta yang dibuatnya berikut dokumen-dokumen yang bersangkutan kepada Kantor Pertanahan untuk didaftar.
- (2) PPAT wajib menyampaikan pemberitahuan tertulis mengenai telah disampaiakannya akta sebagaimana dimaksud pada ayat (1) kepada para pihak yang bersangkutan.

Pasal 42

- (1) Untuk pendaftaran peralihan hak karena pewarisan mengenai bidang tanah hak yang sudah didaftar dan hak milik atas satuan rumah susun sebagai yang diwajibkan menurut ketentuan sebagaimana dimaksud dalam pasal 36, wajib diserahkan oleh yang menerima hak atas tanah atau hak milik atas satuan rumah susun yang bersangkutan sebagai warisan kepada Kantor Pertanahan, sertifikat hak yang bersangkutan, surat kematian orang yang namanya dicatat sebagai pemegang haknya dan surat tanda bukti sebagai ahli waris.

25 MAR 2008

00000778

